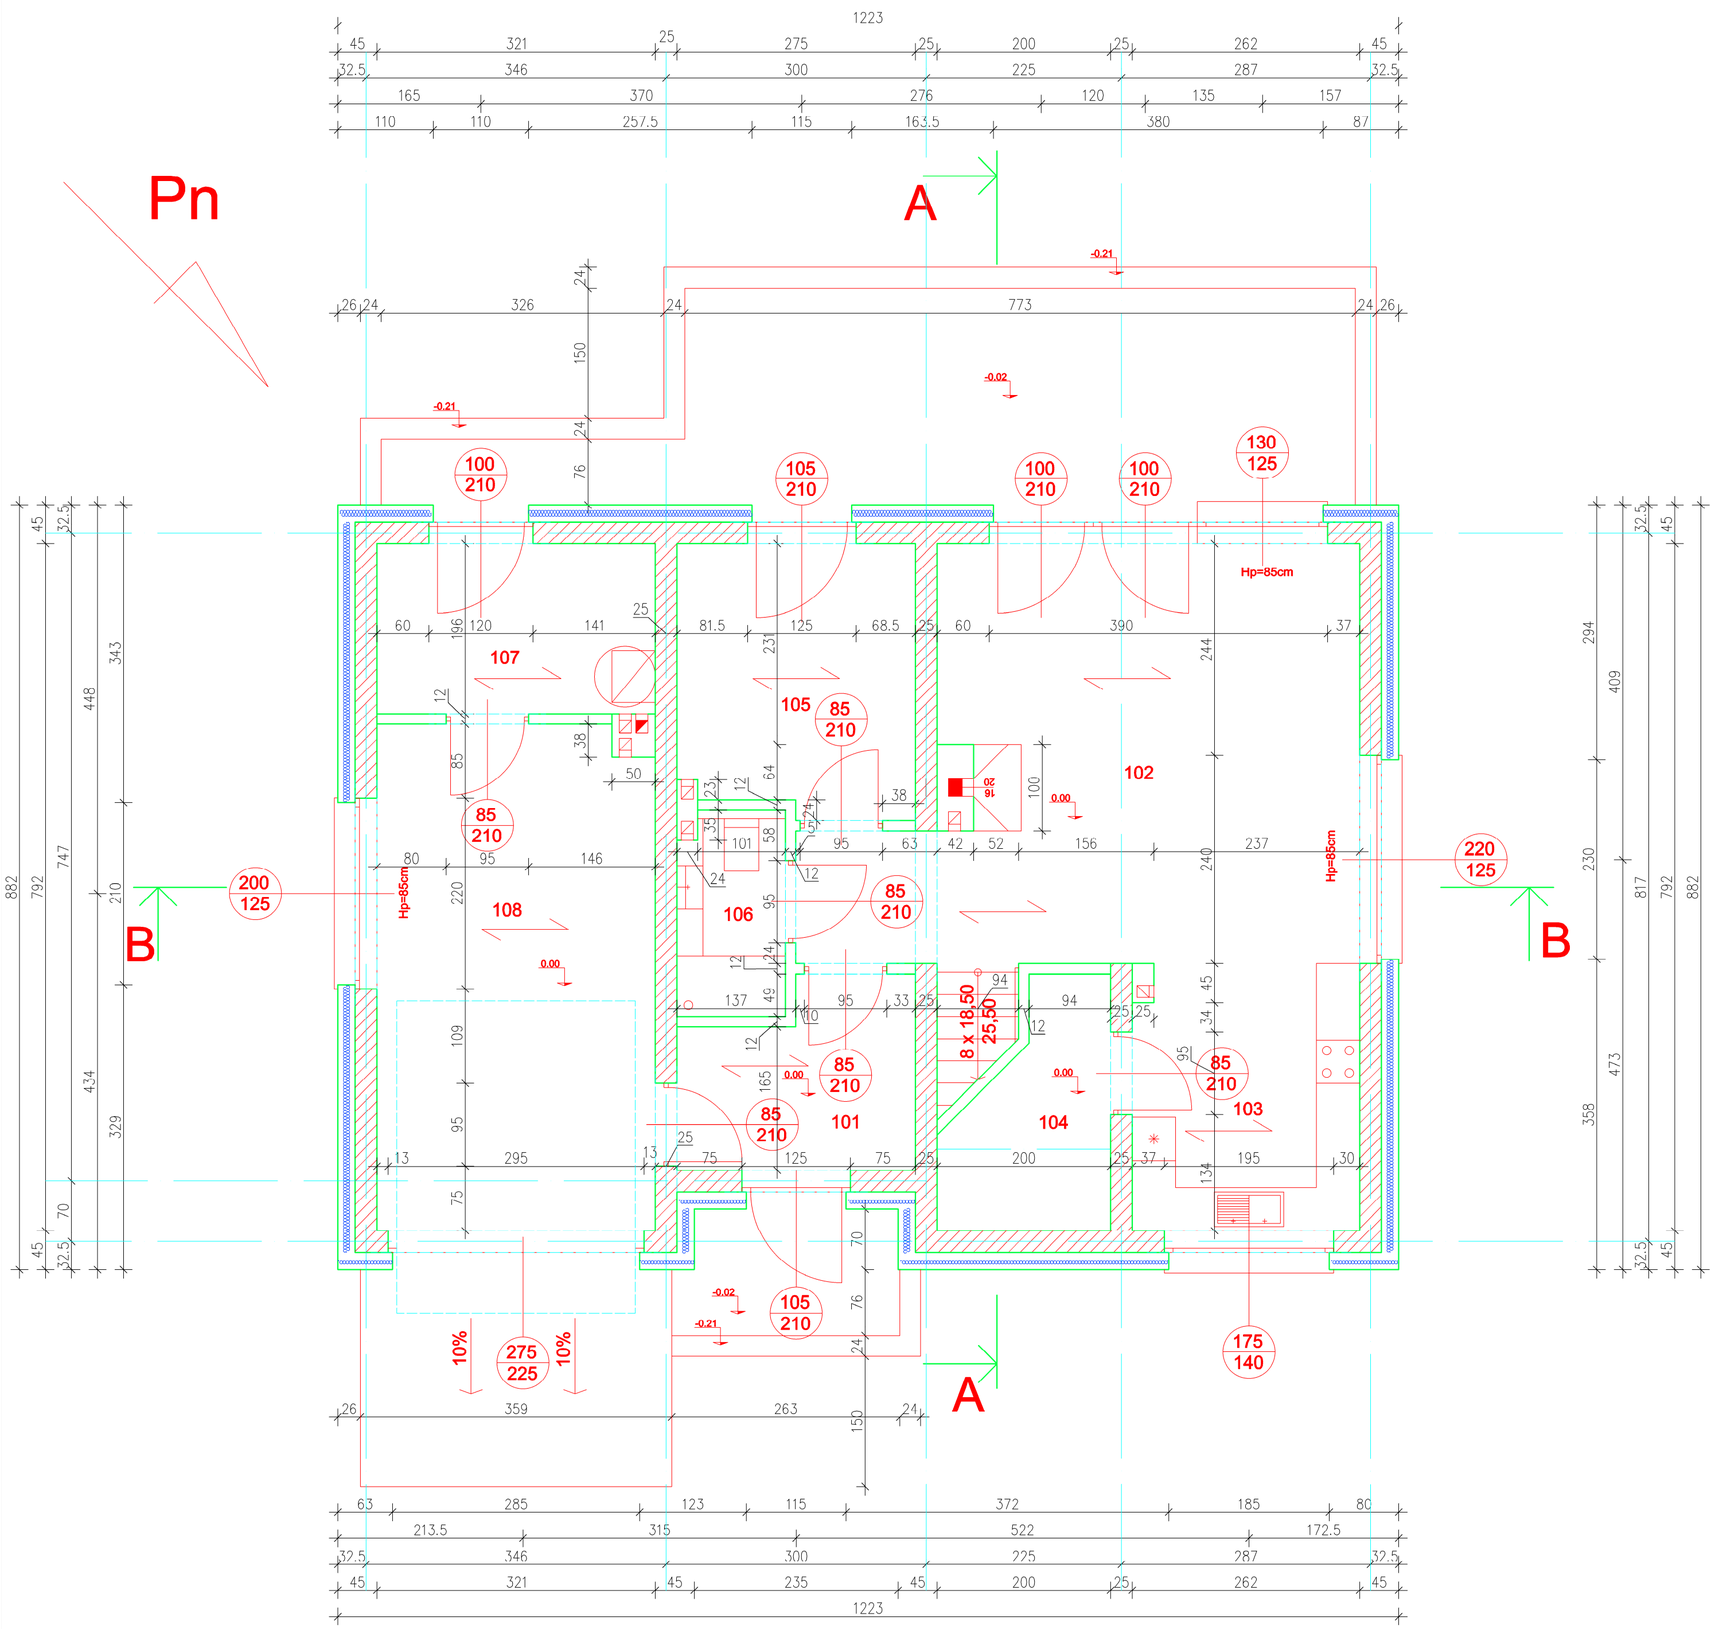

PARTER - ZESTAWIENIE POMIESZCZEŃ			
NUMER	NAZWA	POWIERZCHNIA UŻYTKOWA [m²]	POSADZKA
101	WIATROŁAP	5.38	PANELE
102	SALON	25.64	PANELE
103	KUCHNIA	8.36	PŁYTKI
104	SPIŻARNIA	2.78	PANELE
105	POKÓJ	8.39	PANELE
106	ŁAZIENKA	2.92	PŁYTKI
107	KOTŁOWNIA	6.29	PŁYTKI
108	GARAŻ	18.56	PŁYTKI
RAZEM		78.32	

DOM JEDNORODZINNY			
RUT PARTERU SKALA 1:50			
ADRES	POLITECHNIKA POZNAŃSKA WYDZIAŁ INŻYNIERII LĄDOWEJ I TRANSPORTU		
INWESTOR		ADRES	
PROJEKTANT	PAWEŁ PRZYBYLSKI		DATA
NUMER UPRAWNIEŃ	XXX YYY		NR RYSUNKU A1