PRZEKRÓJ B-B

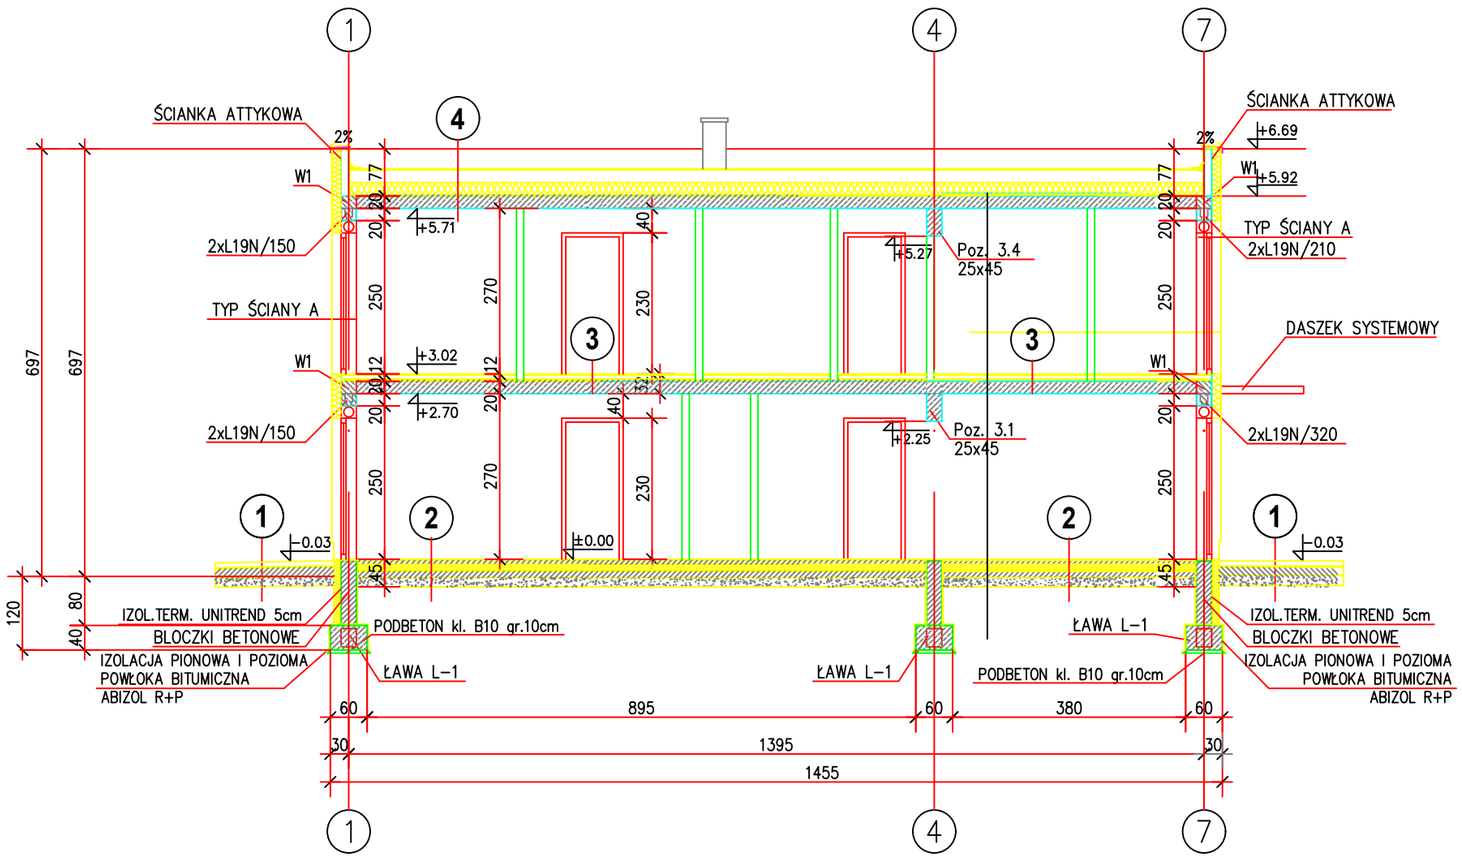

1

Kostka Pozbruk 8 cm
2 x papa na lepiku
Chudy beton 15 cm
Podsypka piaskowa 15 cm
zagęszczona Is=0.95

2

Terakota lub panele drewniane
Posadzka betonowa B20 6 cm
Styropian FS20 10 cm
Papa termozgrzewalna
Podbudowa betonowa B15 10 cm
Podsypka piaskowa 15 cm
zagęszczona Is=0.95

3

Terakota lub panele drewniane
Gładź cementowa 4 cm
Styropian 2 cm
Izolacja –folia PE
Strop żelbetowy gr.18 cm
Tynk cement.–wapienny 1,5 cm

4

Papa termozgrzewalna
Styropian min. gr. 20 cm
Kliny styropianowe
Paroizolacja –folia PE
Strop filigran gr.20 cm
Tynk cement.–wapienny 1,5 cm

A

Tynk cement.–wapienny1.5 cm
Poroterm 25cm
Styropian 15 cm
Tynk systemowy na siatce

B

STYRODUR 8 cm
IZOLACJA – ABIZOL R+G
BLOCZKI BETONOWE 25 cm

UWAGI:

DO OBLICZEŃ ELEMENTÓW PRZYJĘTO NASTĘPUJĄCE WARUNKI GRUNTOWE:
– PIASEK ŚREDNI ŚREDNIO ZAGĘSZCZONY I_D0,5
PO WYKONANIU WYKOPU NALEŻY BEZWZGLĘDNIE ODEBRAĆ PRZEZ UPRAWNIONEGO GEOTECHNIKA PODŁOŻE GRUNTOWE I W PRZYPADKU WYSTĄPIENIA ZMIENNYCH WARUNKÓW GRUNTOWYCH POINFORMOWAĆ PROJEKTANTA
– DO 30 CM PONAD GRUNT BLOCZKI BETONOWE O WYTRZYMAŁOŚCI 10,0 MPa NA ZAPRAWIE MARKI 5MPa
– POWYŻEJ 30 CM PONAD GRUNT PUSTAKI POROTHERM 25P+W O WYTRZYMAŁOŚCI 10MPa NA ZAPRAWIE MARKI 5MPa
– OCIEPLENIE WEŁNĄ MINERALNĄ GR. 15 CM
– BETON KLASY B–20 ; STAL ZBROJENIOWA A–III, A–I St3S PODBETON 10 MPa
FILARKI MIĘDZYOKIENNE WYKONAĆ Z CEGŁY PEŁNEJ O WYTRZYMAŁOŚCI NA ŚCISKANIE 15 MPa, MARKA ZAPRAWY M5
ZBROJENIE PODCIĄGÓW POWIĄZAĆ RAZEM ZE ZBROJENIEM STROPÓW
PODCIĄG WYKONAĆ DWUETAPOWO
– IZOLACJA PIONOWA ŚCIAN I ŁAW FUNDAMENTOWYCH POWŁOKA BITUMICZNA ABIZOL R+P
– IZOLACJA POZIOMA ŁAW FUNDAMENTOWYCH 2x PAPA IZOL.

ZESPÓŁ PROJEKTOWY		
	Imię i nazwisko / Nr uprawnień	Podpis
INWESTOR ZAMAWIAJĄCY		09.2020
		Data
OBIEKT		
STADIUM	PROJEKT BUDOWLANY	PB
BRANŻA	ARCHITEKTURA I KONSTRUKCJA	A i K
1:100	PRZEKRÓJ B–B	7
Skala	Nazwa rysunku	Symbol