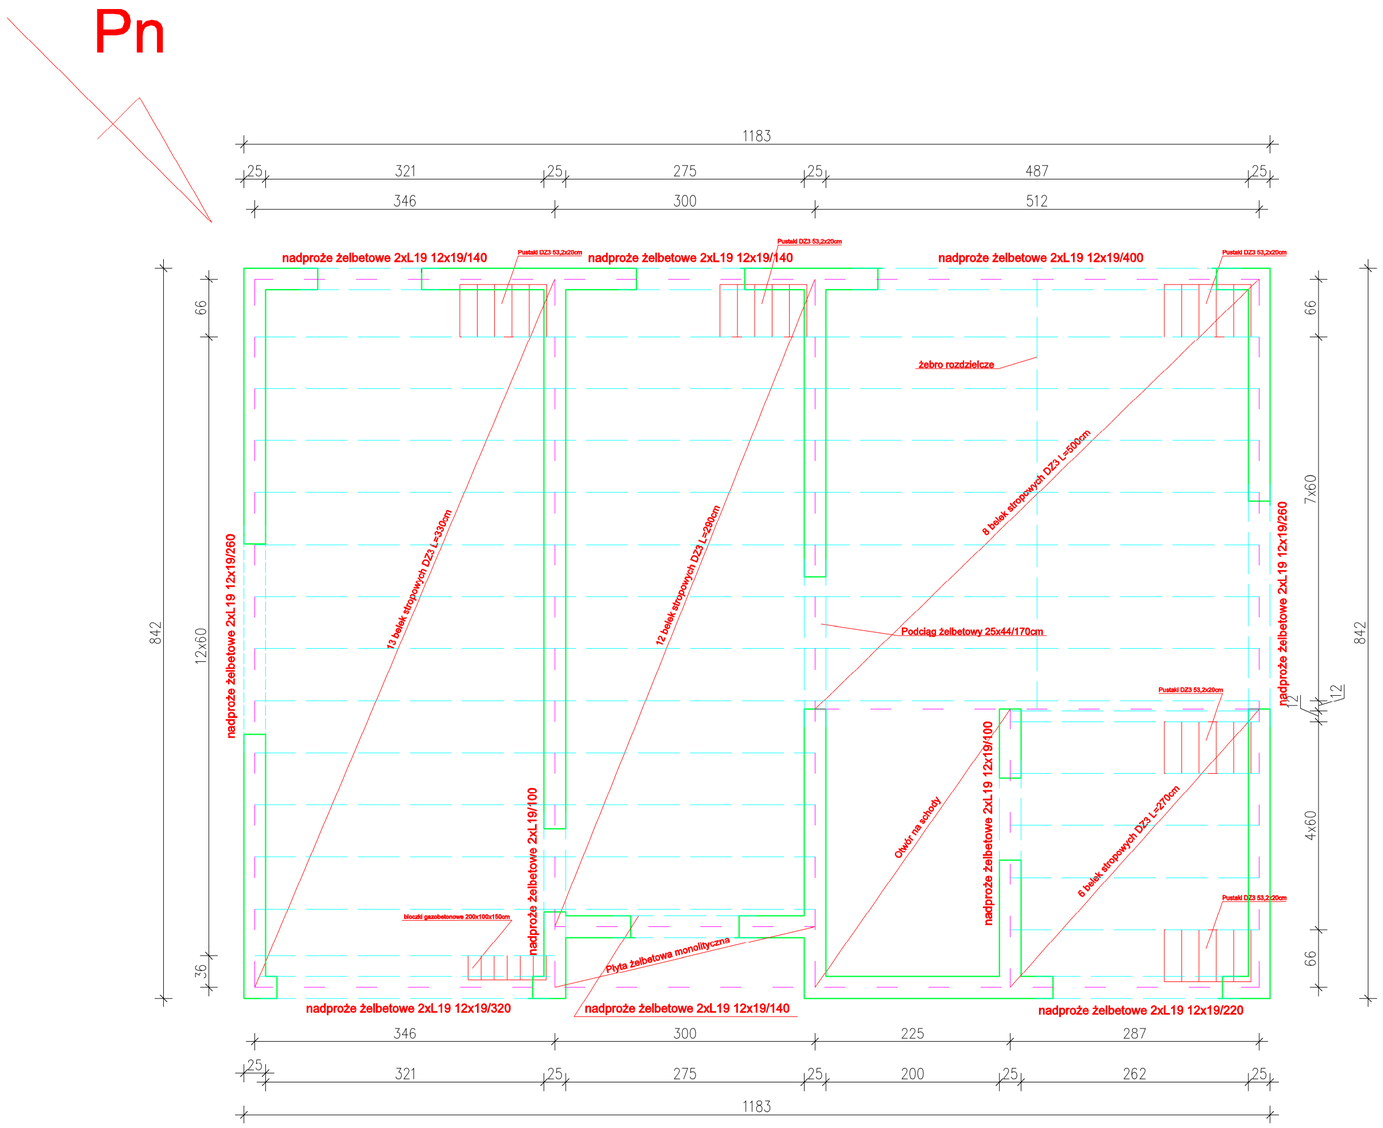

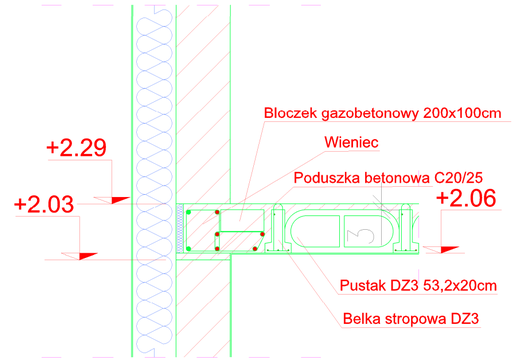

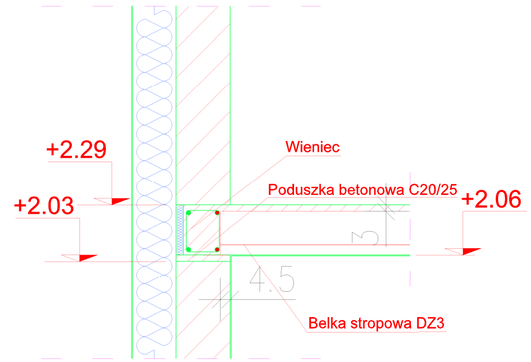

	Zestawienie elementów więźby dachowej
A1	Krokiew C24 10x20x615cm
A2	Krokiew C24 10x20x90cm
A3	Krokiew C24 10x20x420cm
A4	Usztywnienie C24 10x15x170cm
A5	Wzmocnienie C24 3,2x7,5x340cm
A6	Wzmocnienie C24 3,2x7,5x240cm
A7	Wzmocnienie C24 3,2x7,5x650cm
A8	Wzmocnienie C24 3,2x7,5x400cm
A9	Jętka C24 10x15x270cm
A10	Wzmocnienie C24 3,2x7,5x560cm
A11	Wzmocnienie ukośne C24 3,2x7,5x104cm
A12	Wzmocnienie ukośne C24 3,2x7,5x196cm
A13	Murłata C24 15x15x1283cm

DOM JEDNORODZINNY			
RZUT ELEMENTÓW STROPU SKALA 1:50 (szczegóły skala 1:20)			
ADRES	POLITECHNIKA POZNAŃSKA WYDZIAŁ INŻYNIERII LĄDOWEJ I TRANSPORTU		
INWESTOR		ADRES	
PROJEKTANT	PAWEŁ PRZYBYLSKI		DATA
NUMER UPRAWNIEŃ	XXX YYY		NR RYSUNKU A9