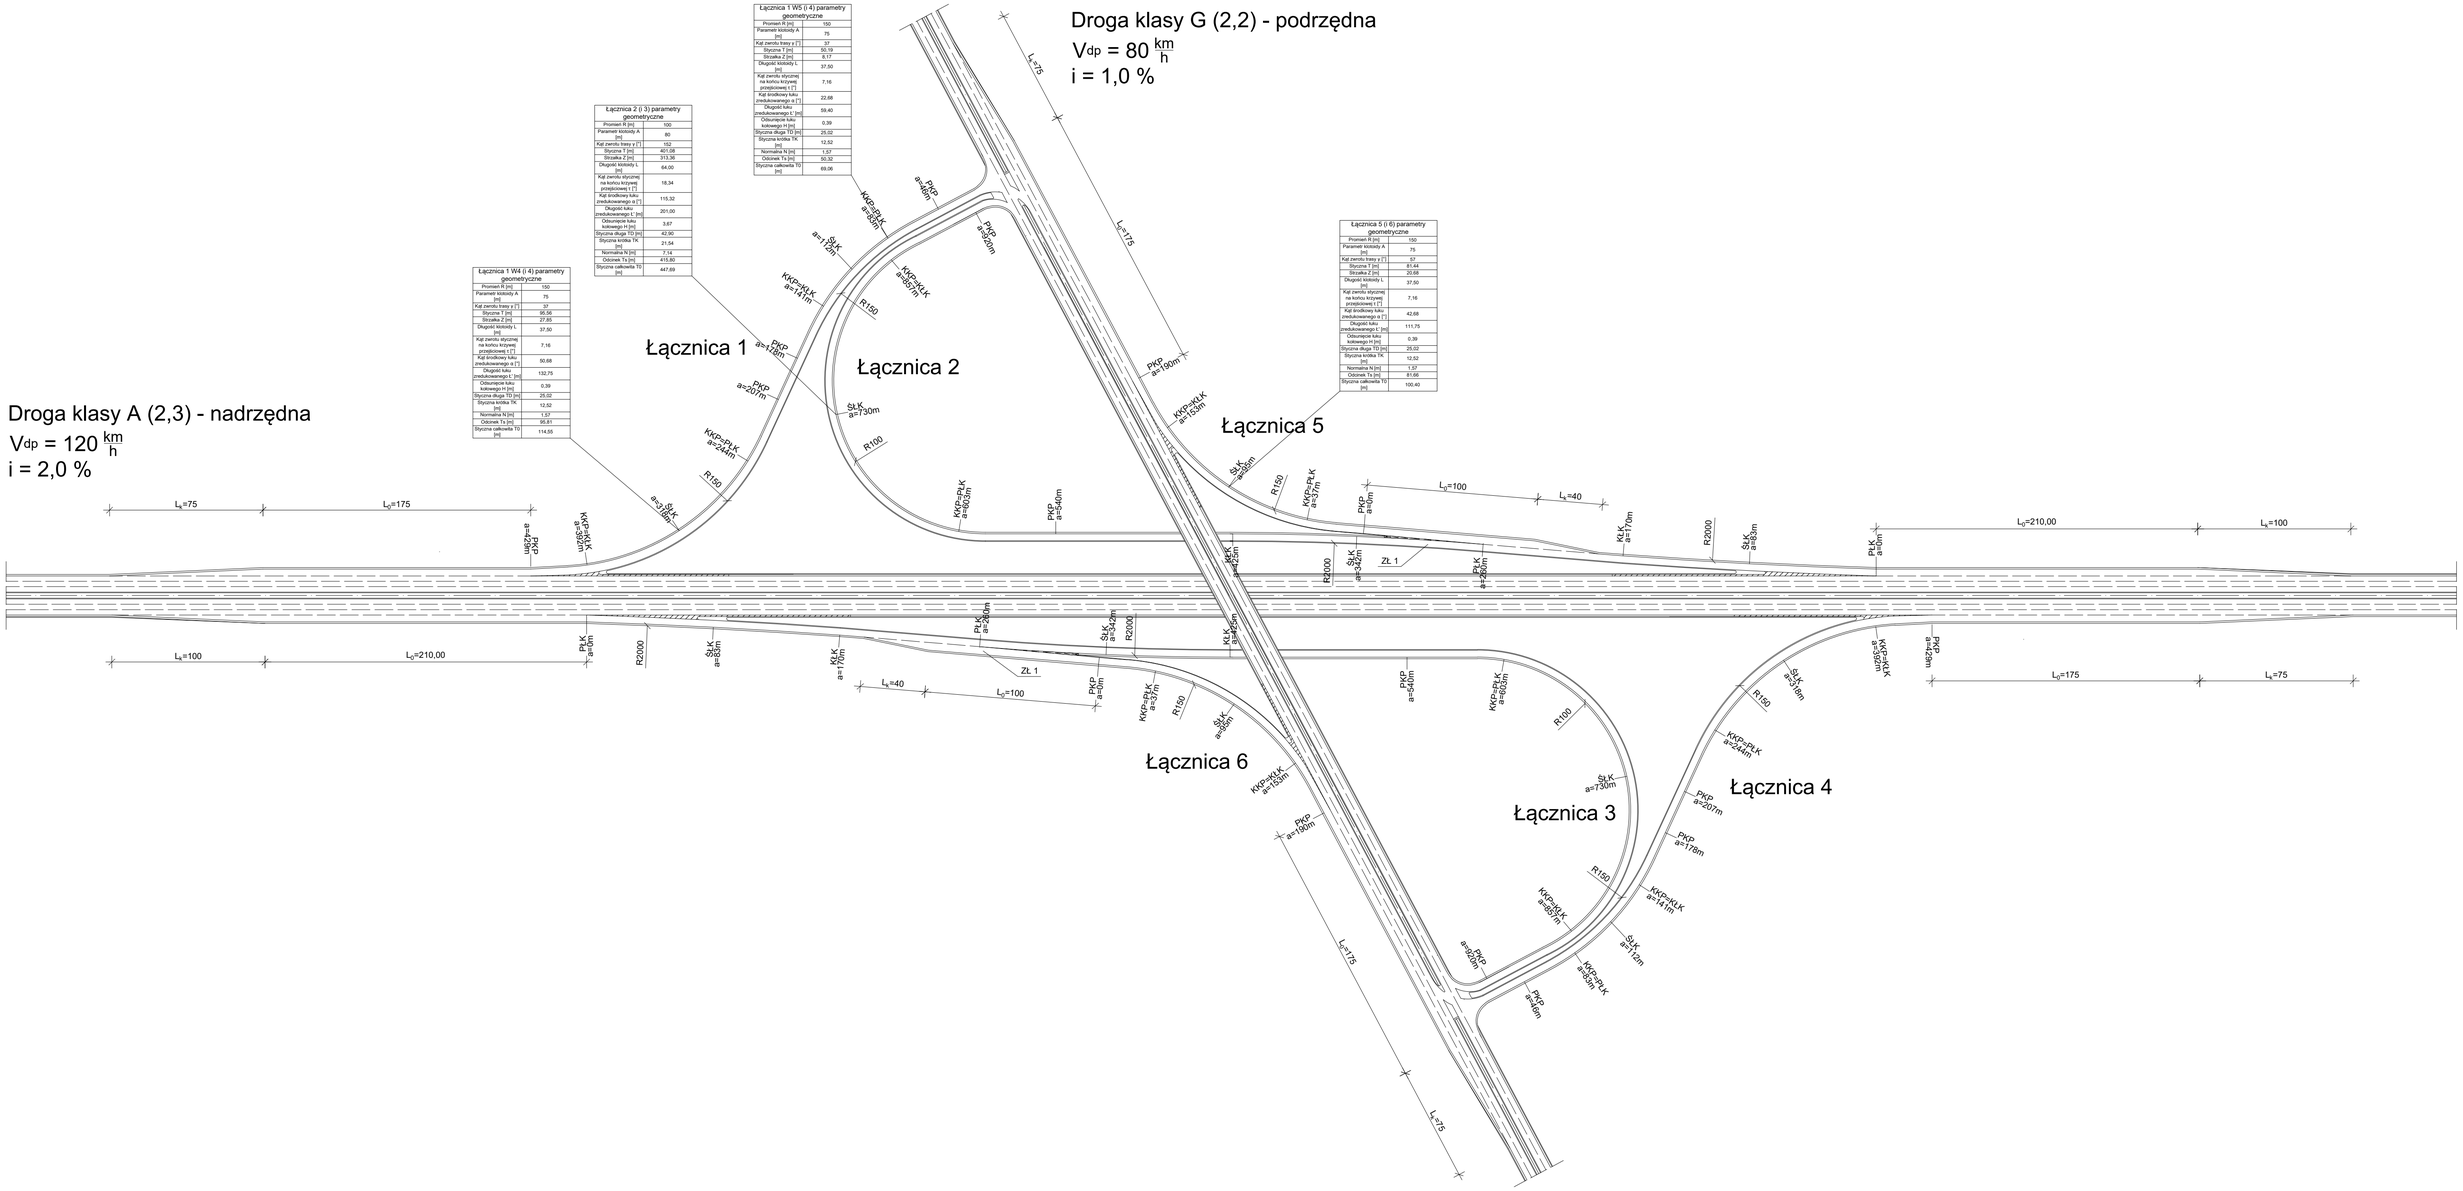

Łącznica 1 W5 (i 4) parametry geometryczne	
Promień R [m]	150
Parametr klotoidy A [m]	75
Kąt zwrotu trasy γ [°]	37
Styczna T [m]	50,19
Strzałka Z [m]	8,17
Długość klotoidy L [m]	37,50
Kąt zwrotu stycznej na końcu krzywej przejściowej τ [°]	7,16
Kąt środkowy łuku zredukowanego ε [°]	22,68
Długość łuku zredukowanego ξ [m]	59,40
Odsunięcie łuku kołowego H [m]	0,39
Styczna długa T0 [m]	25,02
Styczna krótka TK [m]	12,52
Normalna N [m]	1,57
Odcinek Ts [m]	50,32
Styczna całkowita T0 [m]	69,06

Łącznica 2 (i 3) parametry geometryczne	
Promień R [m]	100
Parametr klotoidy A [m]	80
Kąt zwrotu trasy γ [°]	152
Styczna T [m]	401,08
Strzałka Z [m]	313,36
Długość klotoidy L [m]	64,00
Kąt zwrotu stycznej na końcu krzywej przejściowej τ [°]	18,34
Kąt środkowy łuku zredukowanego ε [°]	115,32
Długość łuku zredukowanego ξ [m]	201,00
Odsunięcie łuku kołowego H [m]	3,67
Styczna długa T0 [m]	42,90
Styczna krótka TK [m]	21,54
Normalna N [m]	7,14
Odcinek Ts [m]	415,80
Styczna całkowita T0 [m]	447,69

Łącznica 1 W4 (i 4) parametry geometryczne	
Promień R [m]	150
Parametr klotoidy A [m]	75
Kąt zwrotu trasy γ [°]	37
Styczna T [m]	56,56
Strzałka Z [m]	27,85
Długość klotoidy L [m]	37,50
Kąt zwrotu stycznej na końcu krzywej przejściowej τ [°]	7,16
Kąt środkowy łuku zredukowanego ε [°]	50,68
Długość łuku zredukowanego ξ [m]	132,75
Odsunięcie łuku kołowego H [m]	0,39
Styczna długa T0 [m]	25,02
Styczna krótka TK [m]	12,52
Normalna N [m]	1,57
Odcinek Ts [m]	95,81
Styczna całkowita T0 [m]	114,55

Łącznica 5 (i 6) parametry geometryczne	
Promień R [m]	150
Parametr klotoidy A [m]	75
Kąt zwrotu trasy γ [°]	57
Styczna T [m]	85,44
Strzałka Z [m]	20,68
Długość klotoidy L [m]	37,50
Kąt zwrotu stycznej na końcu krzywej przejściowej τ [°]	7,16
Kąt środkowy łuku zredukowanego ε [°]	42,68
Długość łuku zredukowanego ξ [m]	111,75
Odsunięcie łuku kołowego H [m]	0,39
Styczna długa T0 [m]	25,02
Styczna krótka TK [m]	12,52
Normalna N [m]	1,57
Odcinek Ts [m]	81,66
Styczna całkowita T0 [m]	100,40

Politechnika Poznańska Wydział Inżynierii Lądowej i Transportu Zakład Budownictwa Drogowego		
Opis projektu	Węzeł drogowy typu WB	
Nazwa rysunku	Plan sytuacyjny	Skala 1:2000
Projektował(-ła)	Paweł Przybylski	
Sprawdził(-ła)	mgr inż. Justyna Stróżyk-Weiss	Podpis